
Option 2 – site layout (concept)

Two single-level 2-bed units based on Grey New's 124 Main Street unit plan. One shared driveway from Derwak Street; Unit 1 with carport plus a second space, Unit 2 with two spaces; private courtyards.

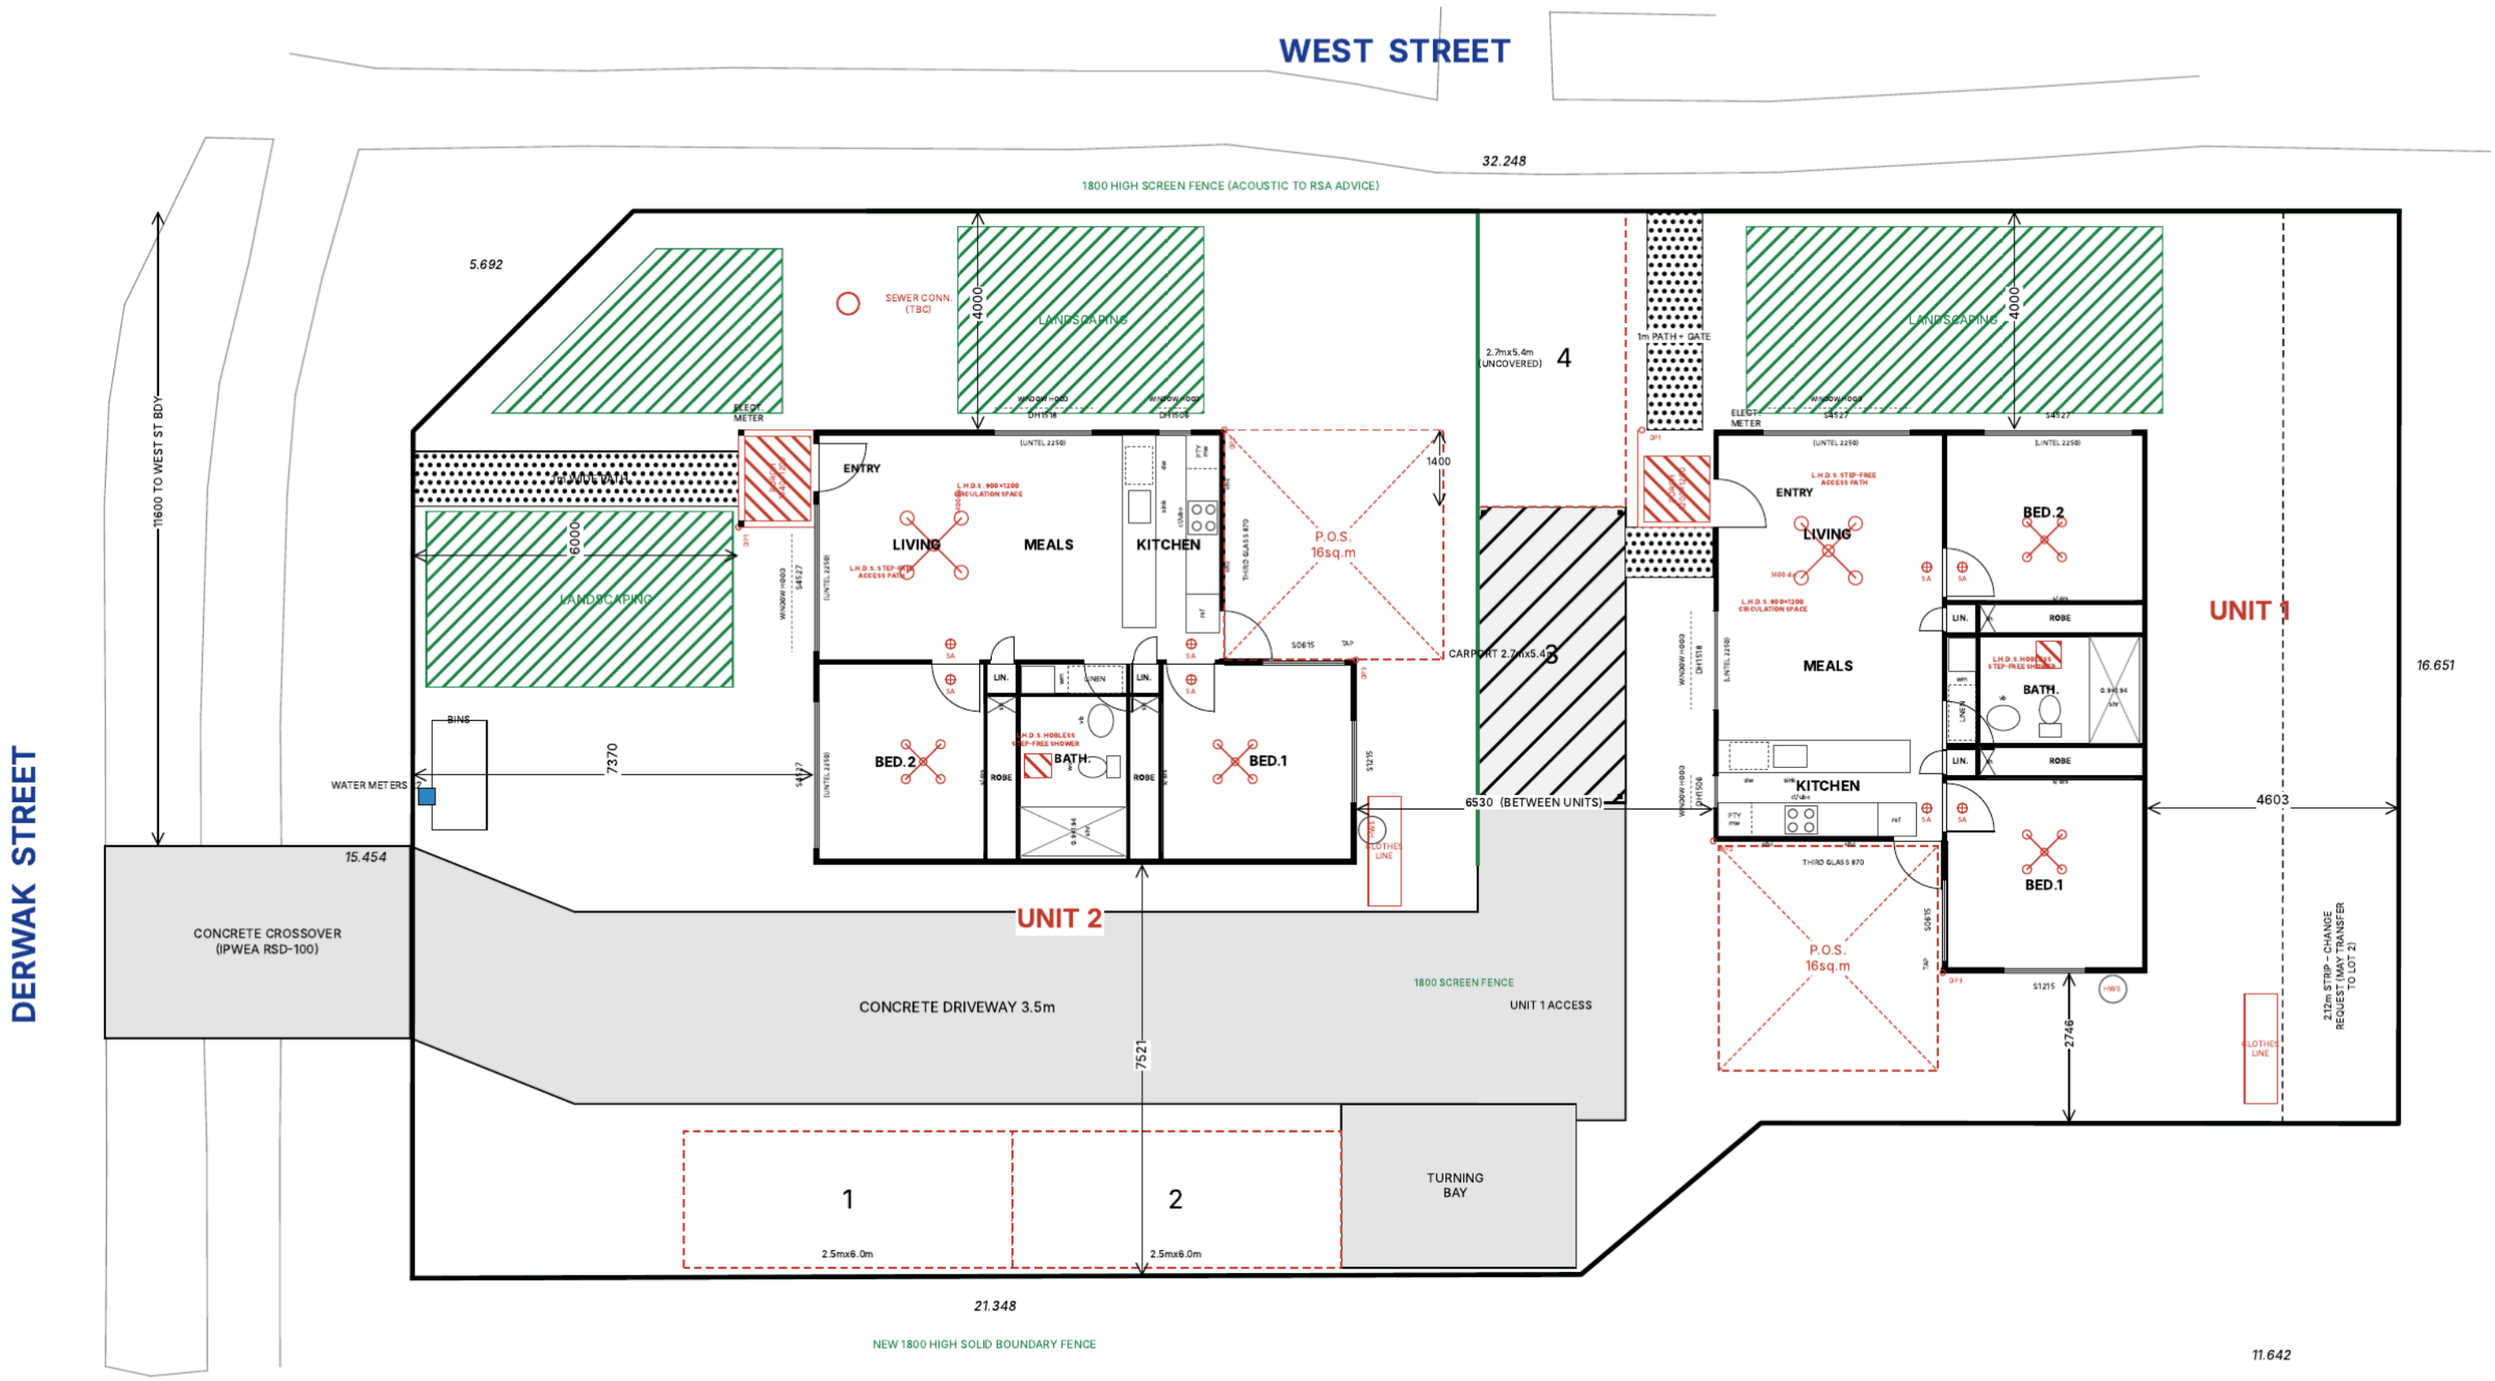


0 5 10 m

SCALE 1:150 @ A3


Option 2 – unit floor plans (concept)

Each unit approx. 68 m² plus a covered porch: two bedrooms with built-ins, open-plan kitchen, living and meals, bathroom with laundry, and a courtyard off the kitchen.

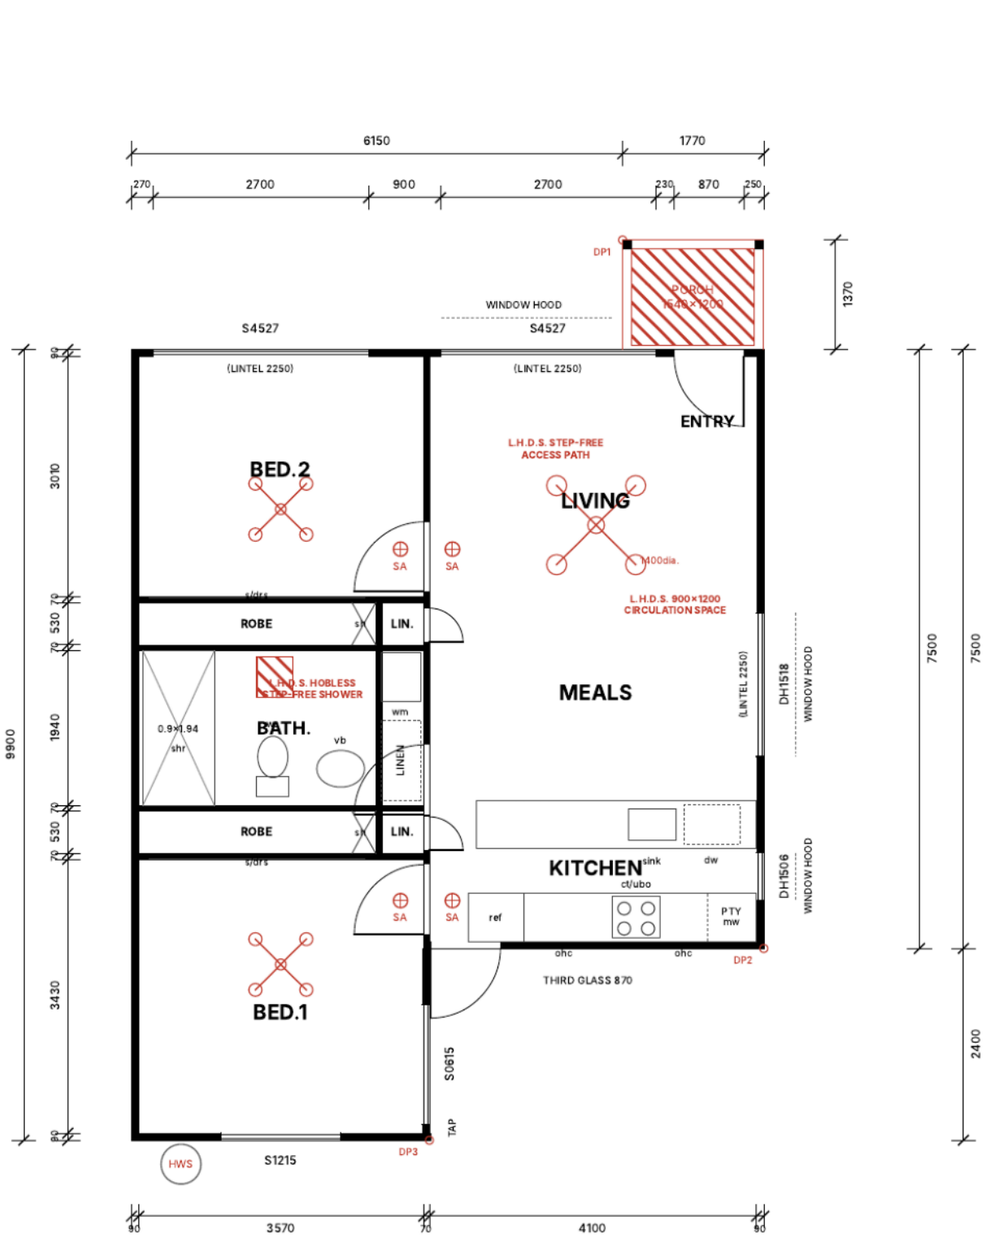

UNIT 2 – FLOOR PLAN 1:100

Type A rotated 180° (highlights to Derwak St) with the entry door and porch moved to the north wall.

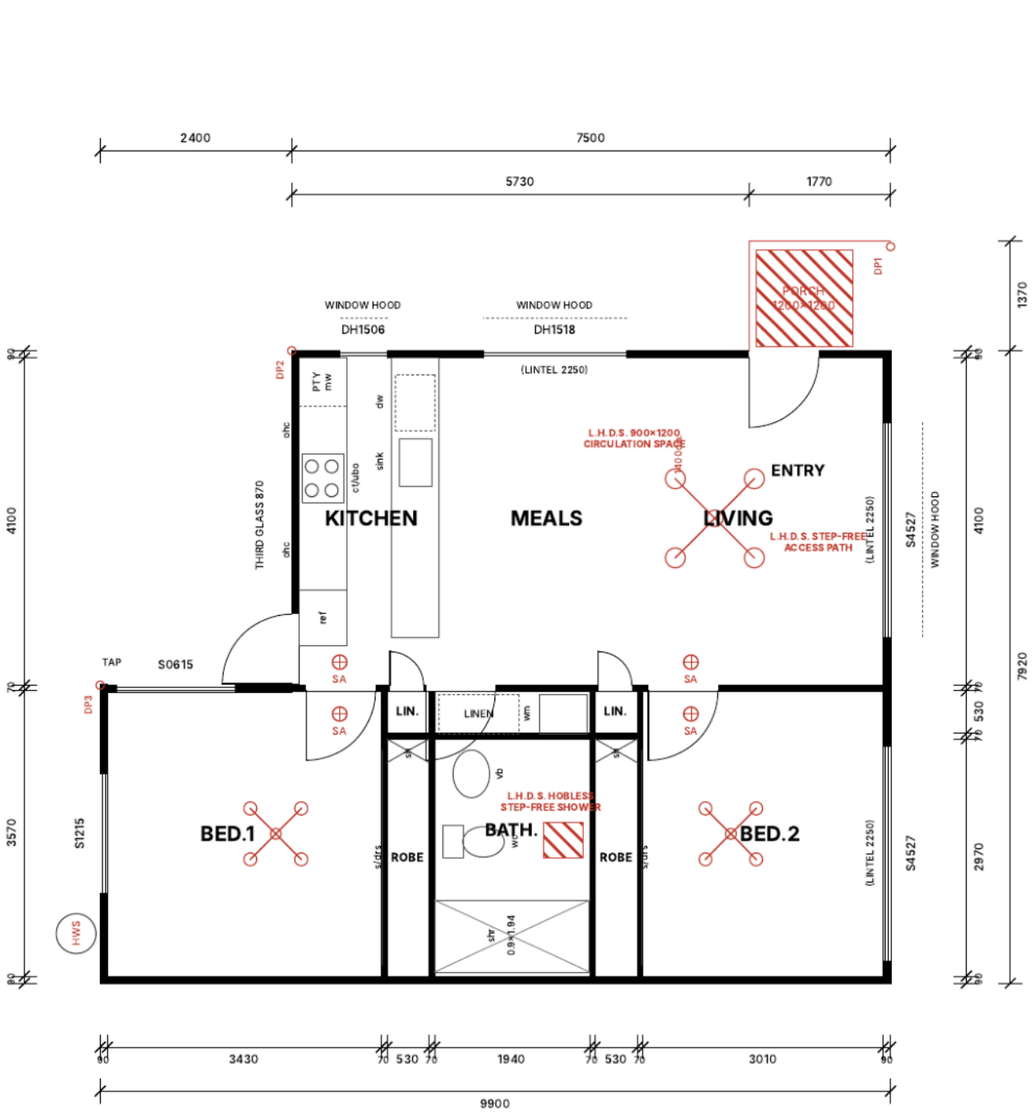

UNIT 1 – FLOOR PLAN 1:100


Type A mirrored. Highlight windows to West St; porch and entry to the north (carport / West St gate).

0 1 2 3 4 5 m


Option 2 – elevations (concept)

Single storey, skillion Colorbond roof with a feature parapet, weatherboard cladding and stone veneer base.


TRANSPORT NOISE CORRIDOR – CHECK SPP MAPPING (WEST ST)

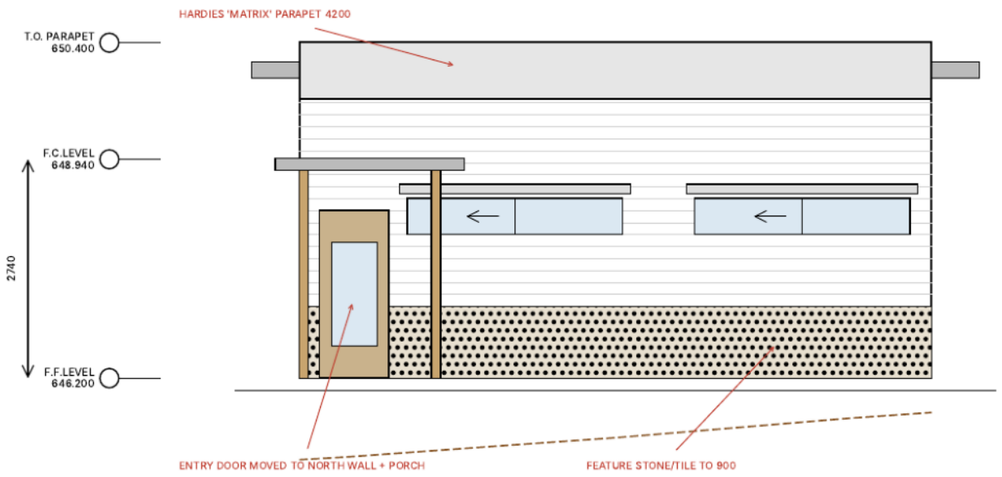


UNIT 2 – ELEVATION TO NORTH (DERWAK STREET)

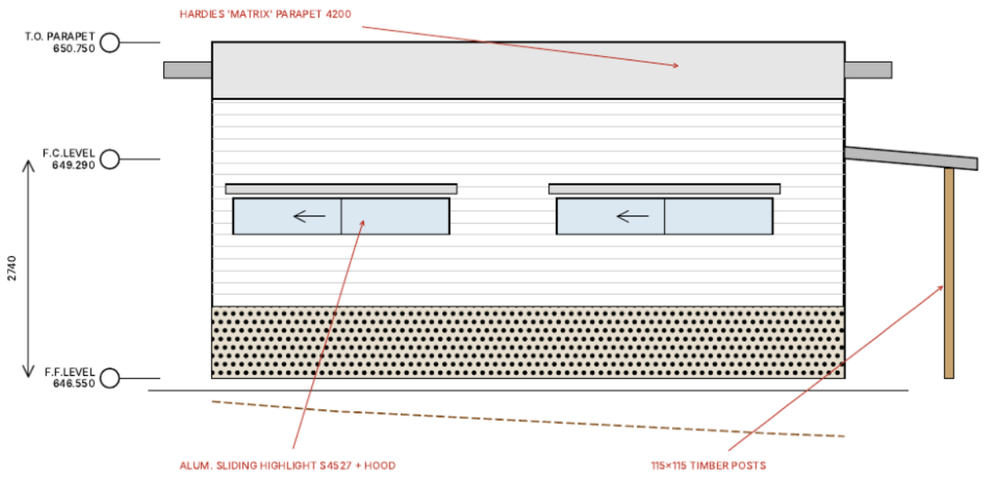


UNIT 1 – ELEVATION TO EAST (WEST STREET)

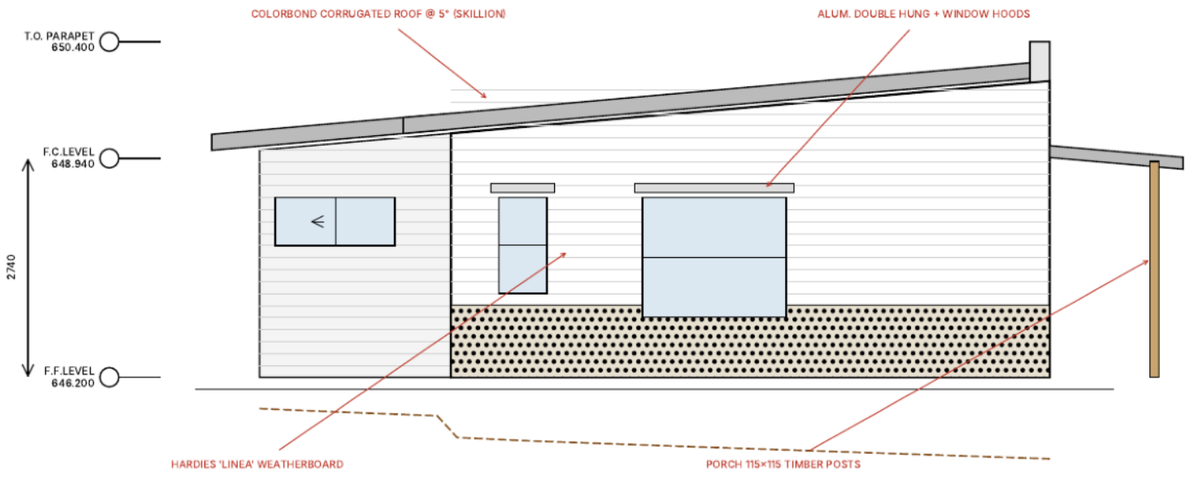


UNIT 2 – ELEVATION TO EAST (WEST STREET)

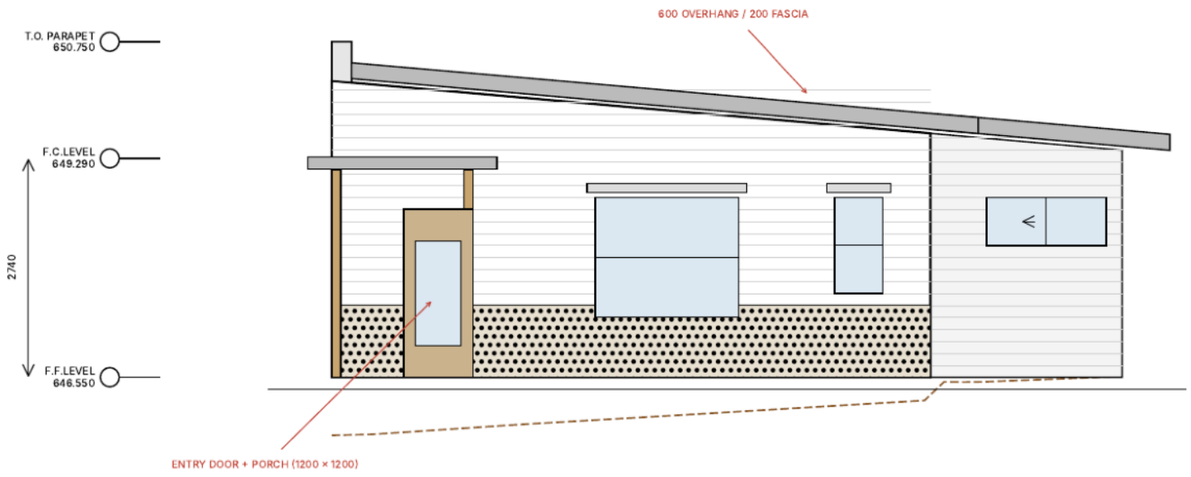


UNIT 1 – ELEVATION TO NORTH (CARPORT)

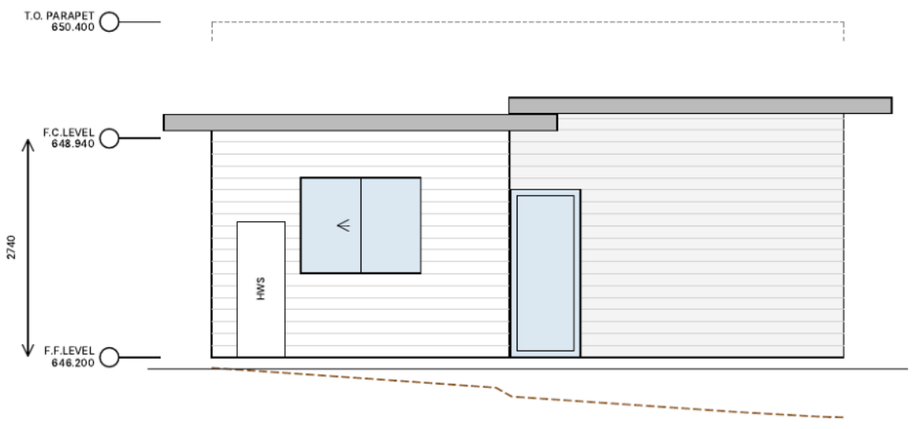


UNIT 2 – ELEVATION TO SOUTH

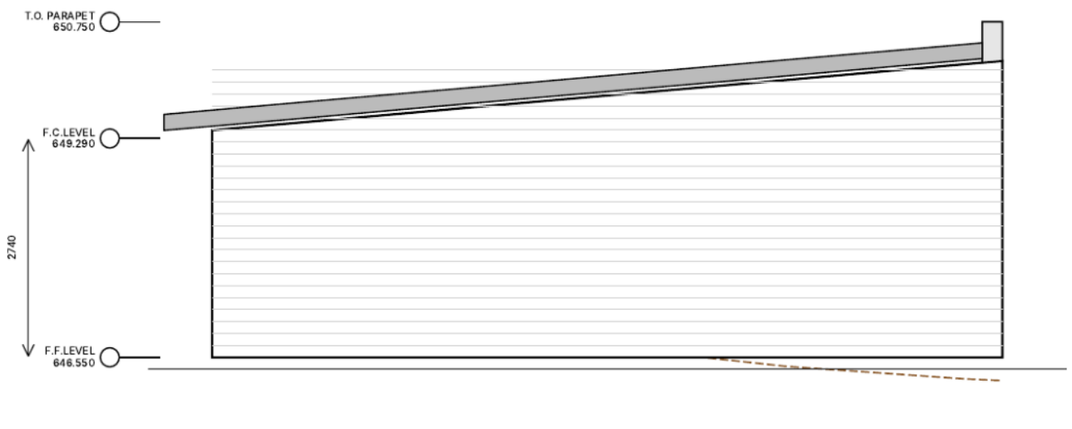

UNIT 1 – ELEVATION TO SOUTH

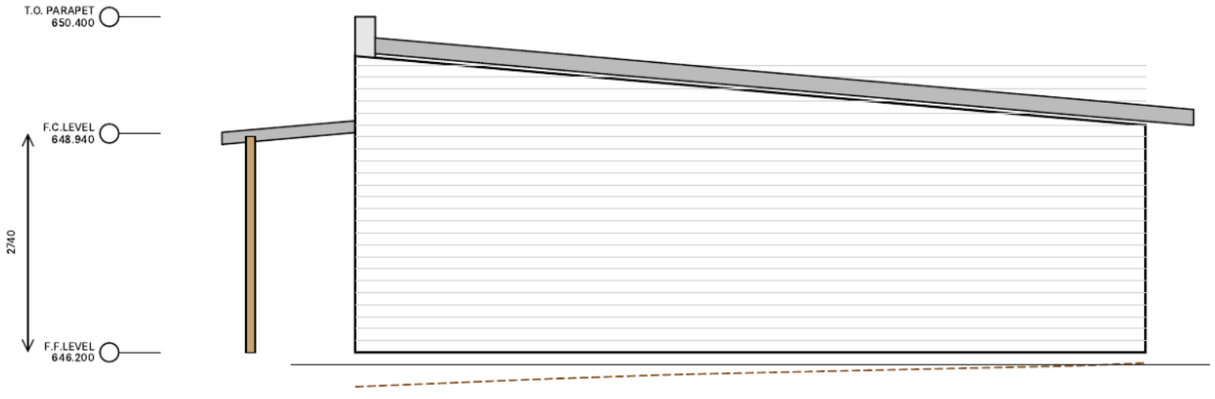

UNIT 2 – ELEVATION TO WEST (DRIVEWAY)

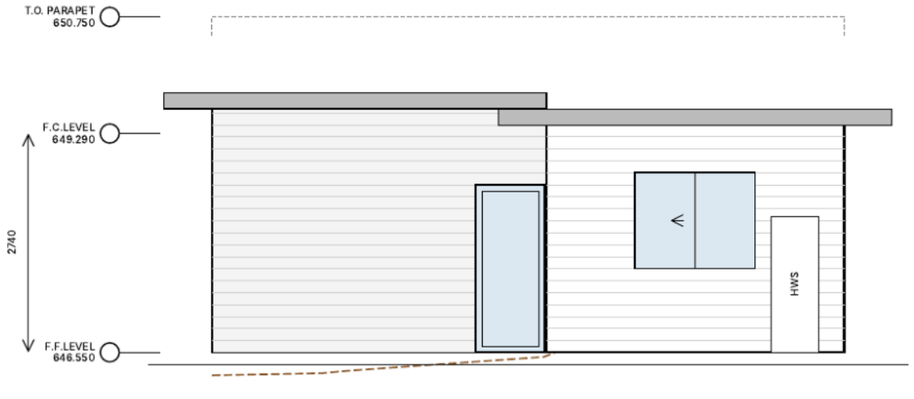

UNIT 1 – ELEVATION TO WEST