

Option 2 – site layout (concept)

Two single-level 2-bed units based on Grey New's 124 Main Street unit plan. One shared driveway from Derwak Street; each unit has a carport plus a second car space; private courtyards.

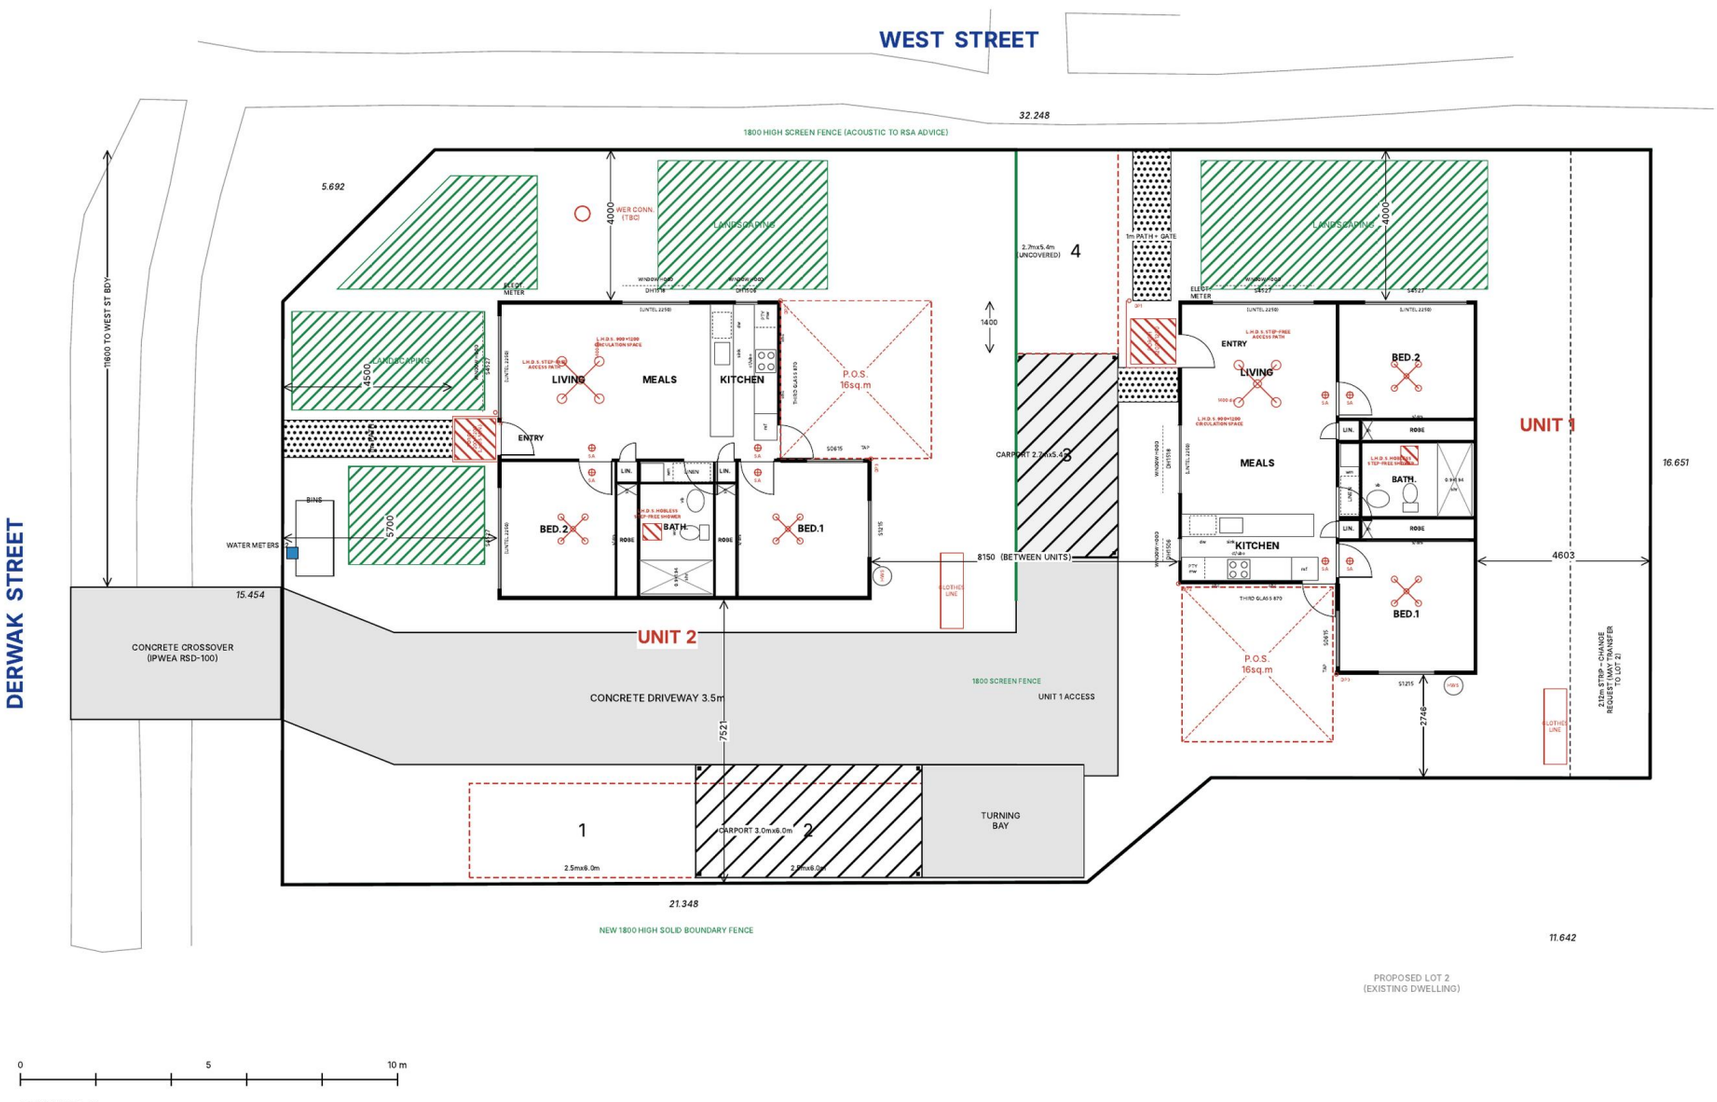


Option 2 – unit floor plans (concept)

Each unit approx. 68 m² plus porch: two bedrooms with built-ins, open-plan kitchen, living and meals, bathroom with laundry, and a courtyard off the kitchen.

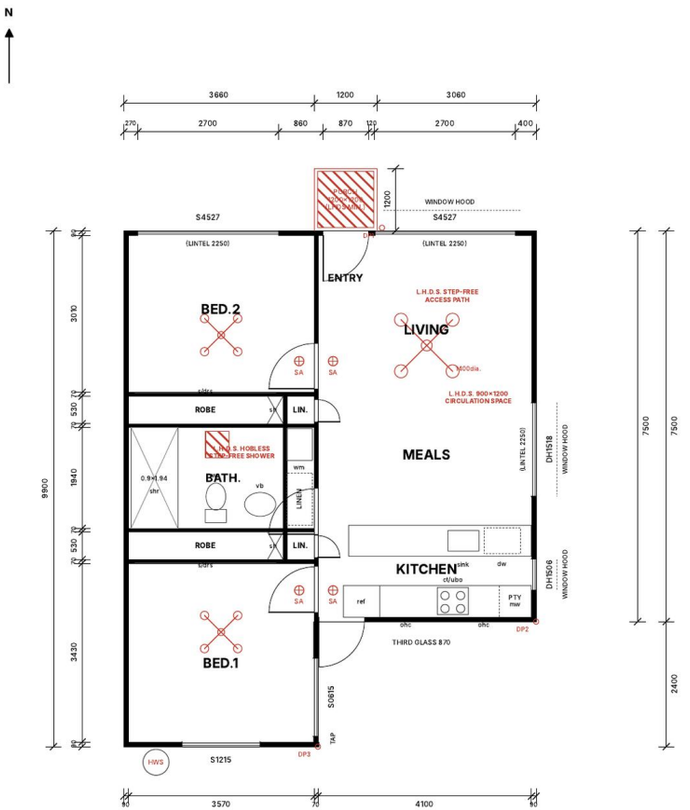

UNIT 2 – FLOOR PLAN 1:100

Type A rotated 180° (highlights to Derwak St); entry door + 1200×1200 LHDS-minimum porch (cantilevered hood) on the north wall at the bed-wing end of the living room.

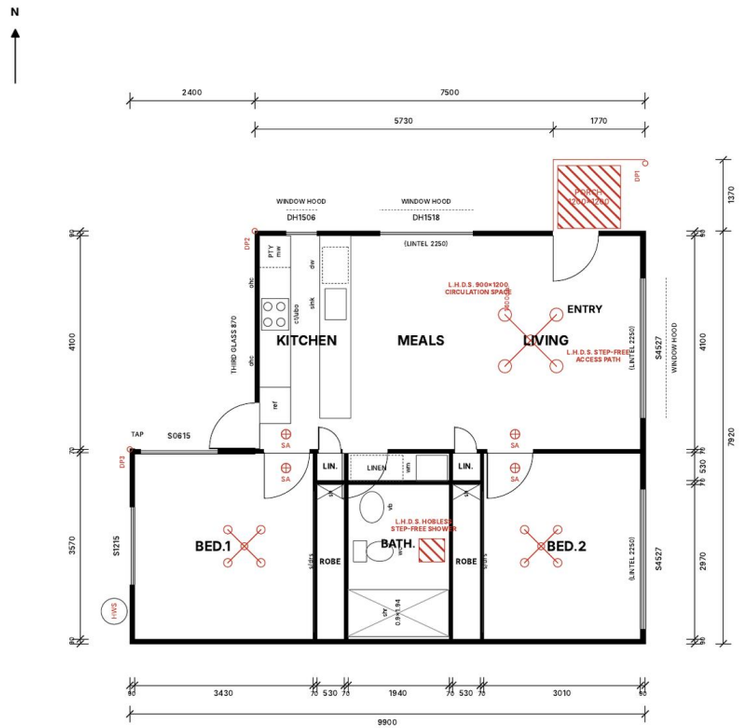

UNIT 1 – FLOOR PLAN 1:100


Type A mirrored. Highlight windows to West St; porch and entry to the north (carport / West St gate).

0 1 2 3 4 5 m


Concept design only – not approved or certified. Subject to detailed design, building certification and Council requirements.

Option 2 – elevations (concept)


Single storey, skillion Colorbond roof with a feature parapet, weatherboard cladding with a feature stone base.

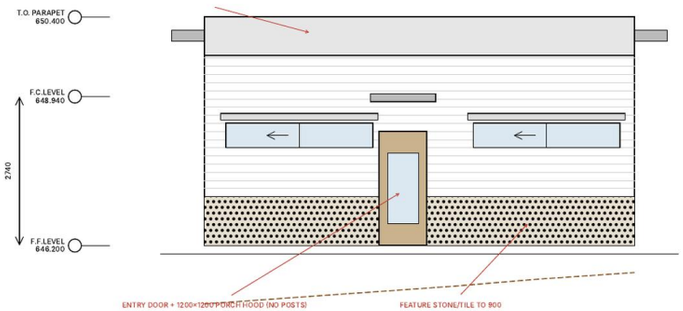


UNIT 2 – ELEVATION TO NORTH (DERWAK STREET)

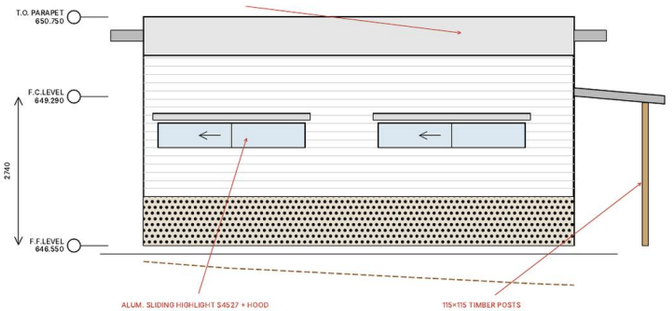

UNIT 1 – ELEVATION TO EAST (WEST STREET)

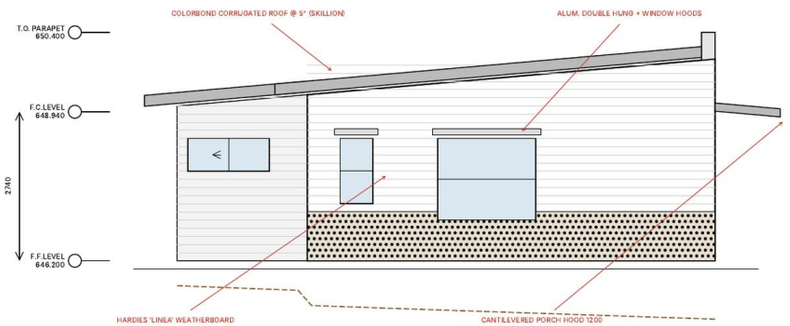


UNIT 2 – ELEVATION TO EAST (WEST STREET)

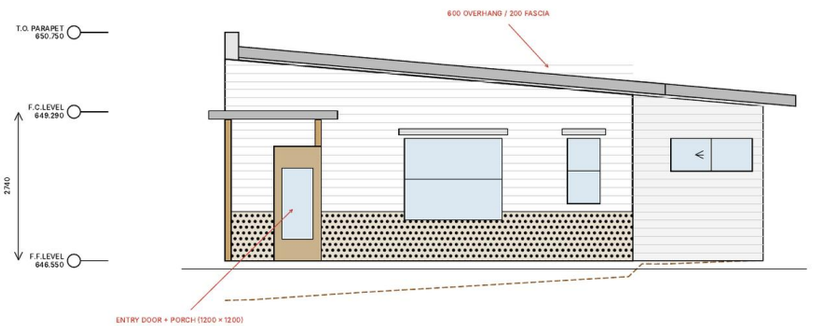


UNIT 1 – ELEVATION TO NORTH (CARPORT)




UNIT 2 – ELEVATION TO SOUTH

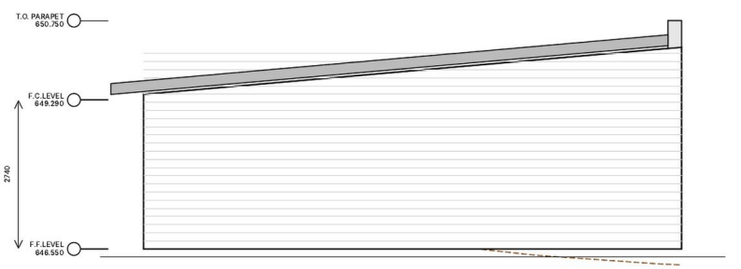

UNIT 1 – ELEVATION TO SOUTH

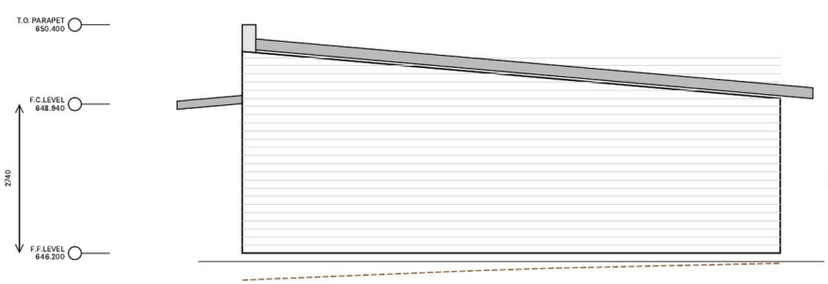

UNIT 2 – ELEVATION TO WEST (DRIVEWAY)

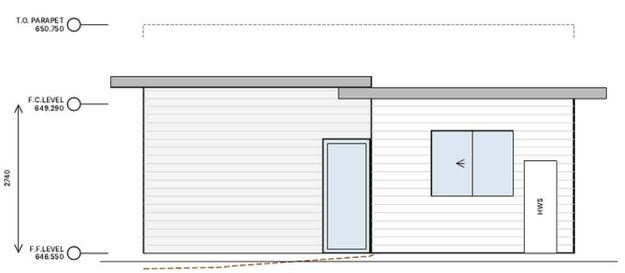

UNIT 1 – ELEVATION TO WEST